# Declaration prealable - Piscine

Parcelle AE 101 - Piscine 1 - Le Vesinet - parcelle AE 101

## Regime d’autorisation

| | |
|---|---|
| Formalite | Declaration prealable (cerfa ndeg 13703)<br>Bassin de 32,0 m2 : de 10 a 100 m2, declaration prealable. |
| Formulaire | cerfa ndeg 13703 (declaration prealable - construction et travaux non soumis a permis de construire portant sur une maison individuelle et/ou ses annexes)<br>A telecharger sur service-public.fr dans sa derniere version, ou a deposer en ligne sur le guichet numerique de la commune. |
| Delai d’instruction | 1 mois (2 mois en secteur protege)<br>A compter du depot complet ; le silence vaut accord, sauf en secteur protege ou une decision expresse est necessaire pour la DP. |
| Taxe d’amenagement | 8 000 EUR de base (250 EUR/m2 x 32,0 m2)<br>Montant = base x (taux communal + taux departemental). Avis dans les 6 mois suivant l’autorisation. |
| Apres les travaux | DAACT, puis declaration fonciere H1 (cerfa ndeg 6650) dans les 90 jours<br>Le bassin entre dans la valeur locative ; declare a temps, il est exonere de taxe fonciere deux ans. |

## Description du projet (notice DP)

Creation d’une piscine enterree de 32,0 m2 de plan d’eau (environ 8,00 x 4,00 m), fond plat, profondeur 1,20 m, volume 38 m3. Structure : coque polyester, gelcoat (coque). Le haut des parois est au niveau du terrain naturel. Margelles de 33 cm en pierre reconstituee ou naturelle. Local technique enterre prefabrique a 5 m du bassin. Dispositif de securite : alarme (nf p90-307). Eau du bassin raccordee a l’assainissement pour les vidanges, pas de rejet au milieu naturel.

Materiaux et couleurs : eau #5bb7e6, margelles #d9d2c3. Terrain : les deblais sont evacues (88 m3) ; aucun mouvement de terre ne modifie le niveau du terrain hors de l’emprise du bassin et de sa plage.

## Aide au remplissage du cerfa 13703

Chaque rubrique du formulaire, avec la valeur lue dans le plan. Les cadres sur le demandeur (identite, adresse, courriel) sont a remplir a la main.

| | |
|---|---|
| Cadre 3 - Terrain : adresse | Le Vesinet<br>Completer le numero, la voie et le code postal. |
| Cadre 3 - References cadastrales | AE 101 - Le Vesinet<br>Prefixe, section et numero de chaque parcelle du terrain. |
| Cadre 3 - Superficie du terrain | 750 m2 |
| Cadre 4 - Nature des travaux | Construction nouvelle : piscine enterree<br>Cocher " piscine " ; preciser le bassin et son local technique. |
| Cadre 4 - Courte description | Piscine enterree de 32,0 m2, coque polyester |
| Cadre 4 - Destination | Habitation (annexe) |
| Cadre 5 - Surface de plancher creee | 0 m2<br>Un bassin ne cree pas de surface de plancher. |
| Cadre 5 - Emprise au sol creee | 32,0 m2<br>Le plan d’eau compte dans l’emprise au sol ; les margelles et une plage au niveau du sol n’en font pas partie. |
| Cadre 5 - Nombre de logements | Sans objet |
| Cadre 6 - Piscine : superficie du bassin | 32,0 m2<br>C’est l’assiette de la taxe d’amenagement (declaration des elements necessaires au calcul des impositions). |
| Cadre 6 - Hauteur hors sol | 0 m (bassin enterre) |
| Cadre 6 - Abri de piscine | Non |
| Cadre 7 - Engagement du demandeur | Date et signature<br>Le dispositif de securite normalise est obligatoire a la mise en eau pour un bassin enterre ou semi-enterre. |

## Pieces du dossier

- [x] DP1 - Plan de situation du terrain - page de ce dossier
- [x] DP2 - Plan de masse cote dans les trois dimensions - page de ce dossier
- [x] DP3 - Plan en coupe precisant l'implantation par rapport au profil du terrain - page de ce dossier
- [ ] DP4 - Plan des facades et des toitures (bassin hors-sol, local technique, abri) - a fournir par le demandeur
- [ ] DP5 - Representation de l'aspect exterieur (si modification visible) - a fournir par le demandeur
- [ ] DP6 - Document graphique d'insertion dans l'environnement - a fournir par le demandeur
- [ ] DP7 - Photographie du terrain dans l'environnement proche - a fournir par le demandeur
- [ ] DP8 - Photographie du terrain dans le paysage lointain - a fournir par le demandeur
- [ ] DP11 - Notice en secteur protege (materiaux, couleurs) - a fournir par le demandeur

Deux exemplaires papier, ou un depot dematerialise. Ajouter un exemplaire par piece en secteur protege.

# DP1 - Plan de situation

Parcelle AE 101

Le Vesinet - 48,89000 N, 2,13000 E

La parcelle du projet est tracee en trait fort ; le bassin en bleu.

A completer par un extrait de carte (IGN, cadastre.gouv.fr) a plus petite echelle.

N

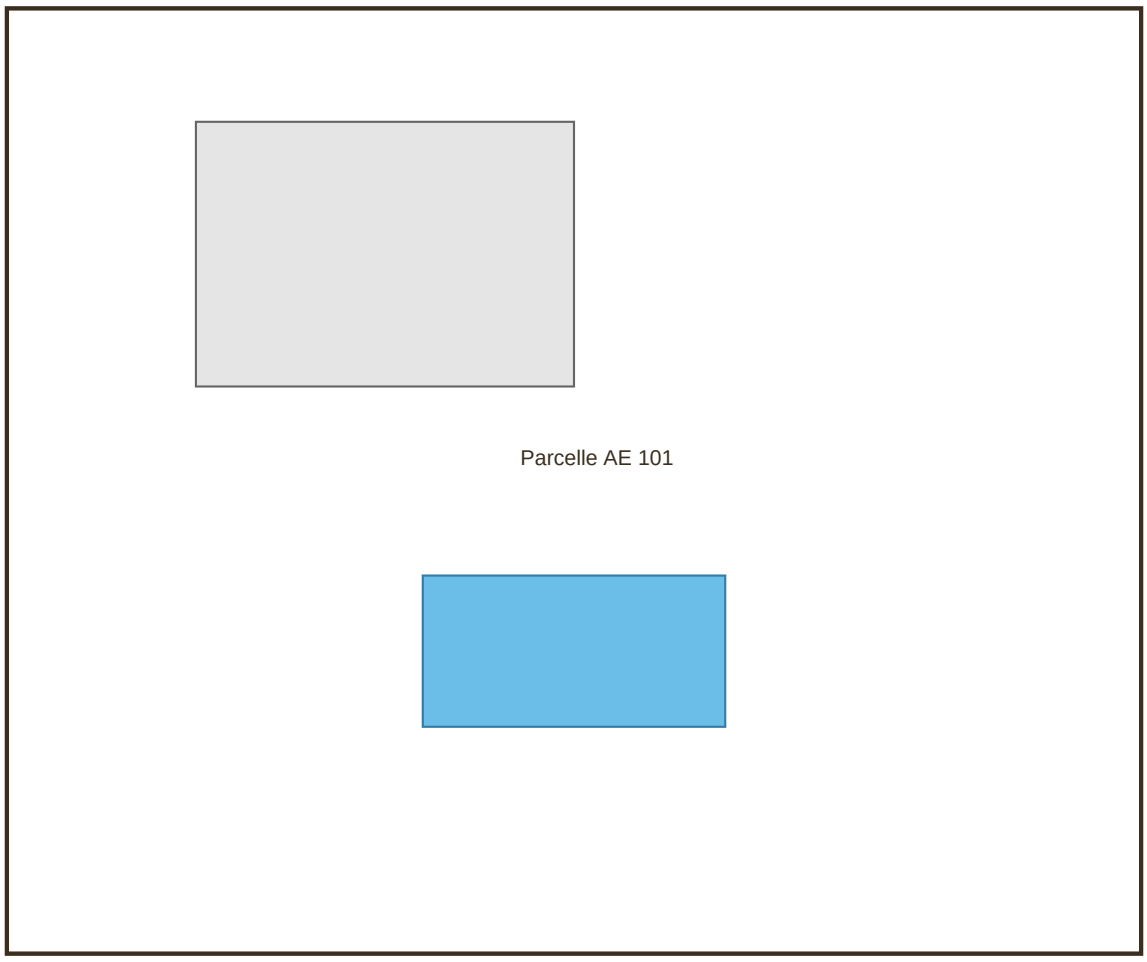


Echelle 1/200

0 10 m

# DP2 - Plan de masse

Parcelle AE 101

Bassin Piscine 1 : 32,0 m2 de plan d'eau, enterree

Distances du bassin aux limites separatives cotees ; cotes de la parcelle en gris.

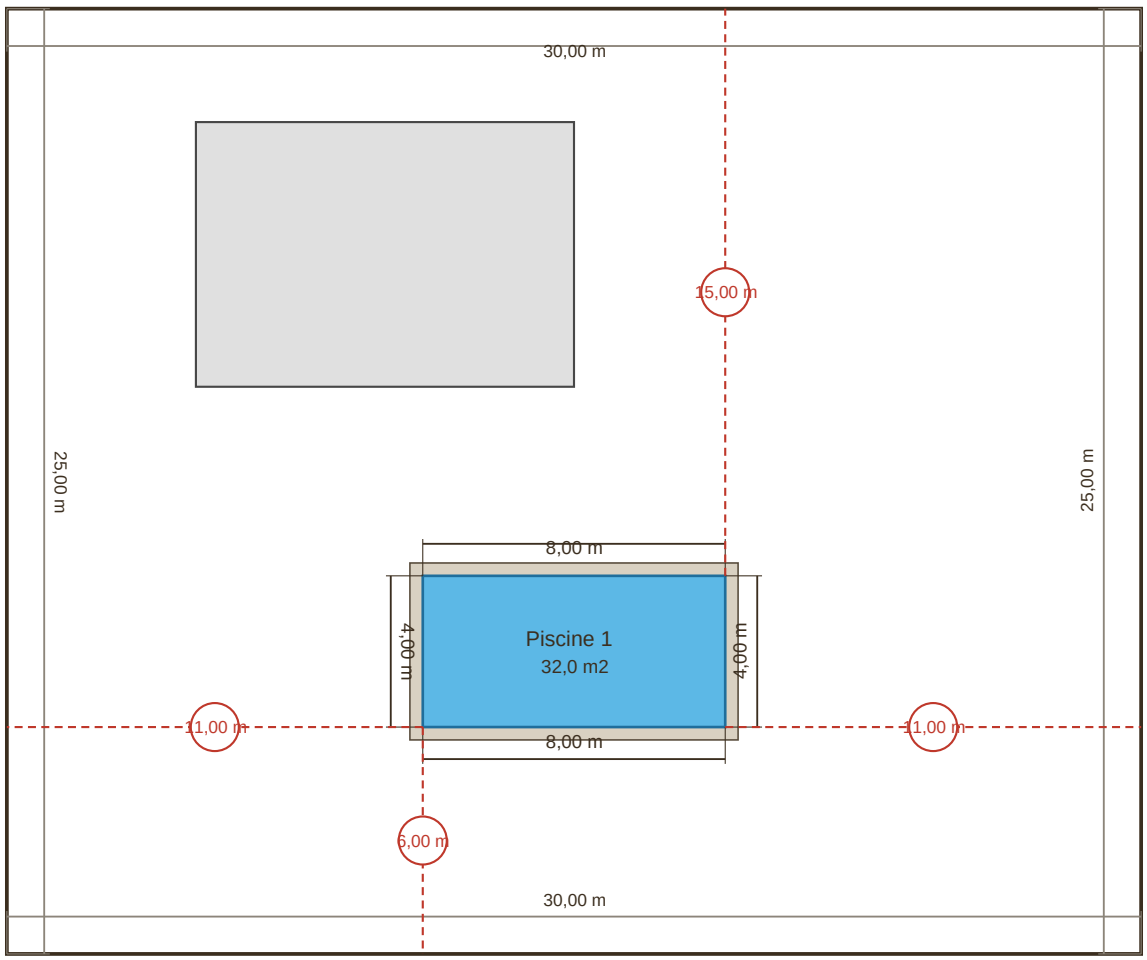


Echelle 1/200

0 — 10 m

## Surfaces et implantation

| | | |
|---|---|---|
| Parcelle | 750 m2 | |
| Plan d'eau (emprise au sol creee) | 32,0 m2 | 32,0 m2 avec le local |
| Margelles | 8,4 m2 | 33 cm |
| Plage | - | |
| Emprise totale (bassin, margelles, plage) | 40,6 m2 | 5,4 % de la parcelle |
| Distance a la limite Sud | 6,00 m | |
| Distance a la limite Est | 11,00 m | |
| Distance a la limite Nord | 15,00 m | |
| Distance a la limite Ouest | 11,00 m | |

# DP3 - Plan en coupe

Piscine 1 - coupe AA selon l’axe du petit bain au grand bain

Terrain naturel en trait fort ; cotes en metres ; echelle 1/75.

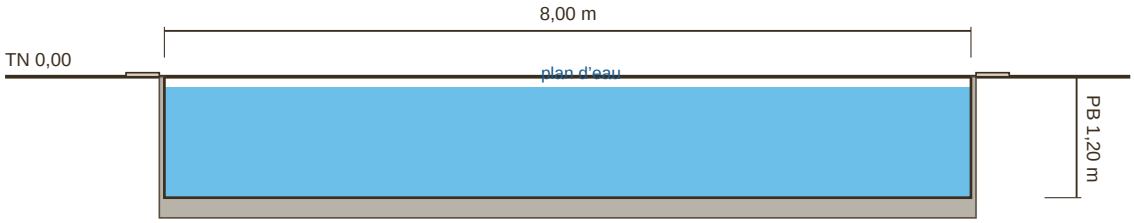


Echelle 1/75

0 2 m

Hauteur des parois 1,30 m (profondeur maximale + revanche 10 cm) ; fouille 1,50 m sous le terrain naturel.

Structure : Coque polyester, gelcoat (coque) ; fond fond plat.

# Pieces a joindre par le demandeur

Insertion et photographies : coller ou imprimer dans les cadres

Ces pieces ne peuvent pas etre produites depuis le plan.

## DP6 - Document graphique d’insertion

Photomontage ou croquis du bassin et de sa plage vus depuis l’espace public ou le jardin, dans leur environnement.

## DP7 - Photographie proche

Le terrain et l’emplacement du bassin, pris depuis la maison ou la limite voisine la plus proche.

## DP8 - Photographie lointaine

Le terrain dans la rue ou le paysage, pris depuis l’espace public.

# Annexe - Note de calcul : Piscine 1

Pre-dimensionnement d'avant-projet, cale sur les usages du metier (temps de recyclage, vitesse de filtration, NF DTU 51.4 pour la plage en bois). Ce n'est ni une etude de sol ni une note de calcul beton : la structure du bassin releve de l'etude d'execution ou de la notice du fabricant.

## 1. Geometrie et volume

| | |
|---|---|
| Implantation | Enterree |
| Plan d'eau | 32,0 m2, perimetre 24,00 m<br>Mesure au nu interieur des parois ; c'est la surface que l'urbanisme compte. |
| Fond | Fond plat : 1,20 m |
| Volume d'eau | 38,4 m3<br>Surface x profondeur. |
| Hauteur des parois | 1,30 m<br>Profondeur maximale + revanche de 10 cm (du plan d'eau au haut des parois). |
| Partie enterree | 1,30 m |

## 2. Terrassement

| | |
|---|---|
| Emprise de la fouille | 45,3 m2<br>Parois de 1 cm plus 50 cm de surlargeur de travail, parois de fouille supposees verticales. |
| Profondeur de fouille | 1,50 m<br>Partie enterree + 20 cm sous le fond (lit de pose en gravier). |
| Deblai | 67,9 m3 |
| Remblai en gravier drainant | 19,6 m3 |
| Evacuation | 88,3 m3<br>Foisonnement de 30 %. |

Sans etude de sol : une nappe haute, un rocher ou un remblai recent changent la fouille, le drainage et le fond (plot de lestage, vide sanitaire, puits de decompression).

## 3. Structure du bassin

| | |
|---|---|
| Structure | Coque polyester, gelcoat (coque) |
| Pression de l'eau au fond | 11,8 kPa<br>rho.g.h, avec h la profondeur maximale. |
| Poussee de l'eau sur une paroi | 8,3 kN par metre de paroi<br>rho.g.h2/2 sur la hauteur de paroi ; la poussee des terres s'y oppose bassin plein et s'exerce seule bassin vide. |
| Pose | Lit de gravier de 20 cm, remblai en gravier roule<br>Remblayer par couches en meme temps que la mise en eau : la coque ne tient que remplie et soutenue. |

Pre-dimensionnement d'avant-projet : le beton, le ferraillage et le drainage relevent d'une etude d'execution (DTU 65.11 reservoirs, Eurocode 2) et de la notice du fabricant pour une coque ou un kit.

## 4. Abords

| | |
|---|---|
| Margelles | 25,4 ml de 33 cm (51 pieces de 50 cm) |
| Plage | Aucune (gazon, gravier) |

## 5. Hydraulique et filtration

| | |
|---|---|
| Temps de recyclage | 4 h<br>Le volume passe entierement au filtre en ce temps. |
| Debit de filtration | 9,6 m3/h<br>Volume / temps de recyclage. |
| Filtre a sable | diam.  500 mm (0,19 m2 de section necessaires)<br>Vitesse de filtration de 50 m/h ; diametre du commerce immediatement superieur. |

| | |
|---|---|
| Pompe | 0,75 CV |
| Skimmers | 2 (un pour 25 m2)<br>Face aux vents dominants ; en hors-sol, un skimmer flottant ou de kit. |
| Refoulements | 3 buses (une pour 15 m2, deux au moins) |
| Bonde de fond, prise balai | 1 et 1<br>La bonde au point bas du grand bain. |
| Canalisations | PVC pression diam.  50 mm, 59 ml<br>Local technique a 5,00 m ; un circuit par piece a sceller, plus le tour du bassin. |

## 6. Equipements

| | |
|---|---|
| Local technique | Local technique enterre prefabrique |
| Eclairage | 2 projecteur(s) LED 12 V (un pour 25 m2) |
| Traitement | Chlore |
| Chauffage | Aucun |

## 7. Securite et reglementation

| | |
|---|---|
| Securite | Alarme (NF P90-307) - 1 u<br>Obligatoire pour tout bassin enterre ou semi-enterre non clos (loi du 3 janvier 2003, art. L.128-1 du CCH). Un bassin hors-sol en est dispense mais reste conseille. |
| Autorisation d’urbanisme | Declaration prealable (cerfa ndeg 13703)<br>Aucune formalite jusqu’a 10 m2 hors secteur protege ; declaration prealable de 10 a 100 m2 (et pour un bassin hors-sol installe plus de trois mois par an) ; permis au-dela de 100 m2 ou avec un abri de plus de 1,80 m. |
| Distances aux limites | Sud : 6,00 m ; Est : 11,00 m ; Nord : 15,00 m ; Ouest : 11,00 m<br>A comparer au reglement de zone du PLU (souvent 3 m, parfois 1 m ou plus) et au Code civil (vues). |
| Taxe d’amenagement | 8 000 EUR de base<br>250 EUR/m2 de plan d’eau, a multiplier par les taux communal et departemental (de 1 a 5 %, plus 2,5 % au plus). |
| Apres les travaux | Declaration d’achevement (DAACT) et declaration fonciere H1 (cerfa ndeg 6650) dans les 90 jours<br>Le bassin entre dans la taxe fonciere ; une exoneration de deux ans suit la declaration faite a temps. |