Plan de masse

Parcelle AE 101

Parcelle AE 101 - Le Vesinet

Surface parcelle : 723,0 m2

2 terrasse(s) au dossier : S1 Terrasse, S2 Table

N

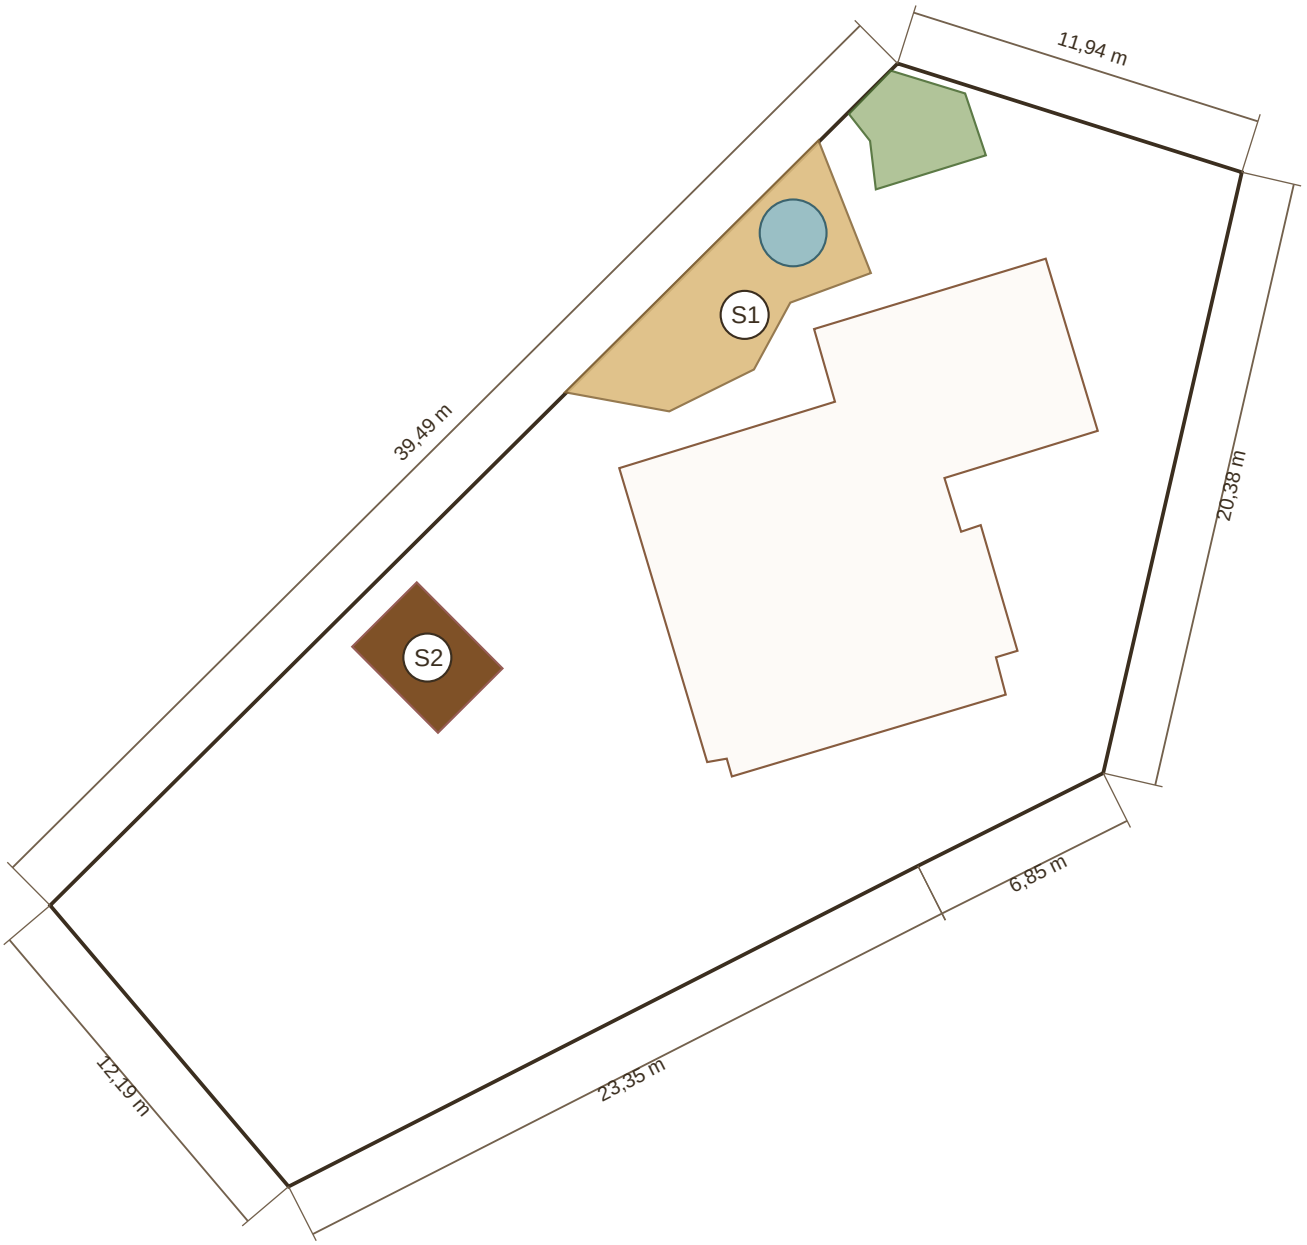

Echelle 1/250

0 10 m

Genere le 28/09/2026 - dimensions en metres, X+ = Est, Y+ = Nord - Plan interactif v5.0.0

Section 1 / 2 - Terrasse

Surface 35,01 m2 - perimetre 28,51 m - pin-classe4

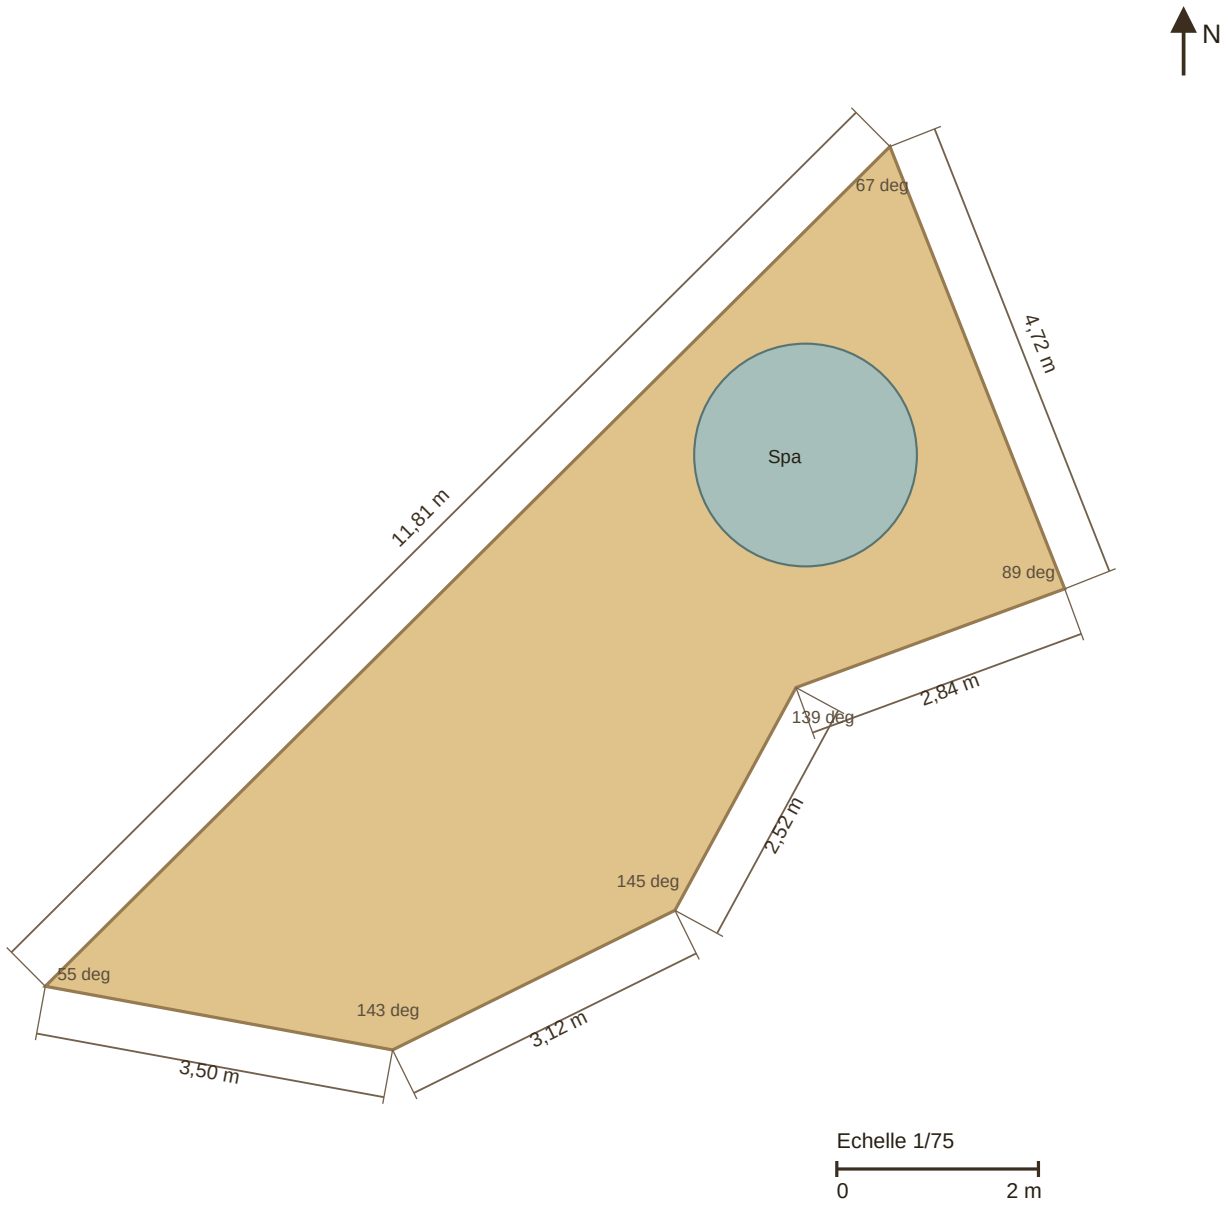

Dimensions

Element	Cote / emprise	Surface	Angle au depart
Cote 1	4,72 m		67 deg
Cote 2	2,84 m		89 deg
Cote 5	2,52 m		139 deg
Cote 3	3,12 m		145 deg
Cote 6	3,50 m		143 deg
Cote 4	11,81 m		55 deg
Terrasse Terrasse	perimetre 28,51 m	35,01 m2	6 sommets
Spa	diametre 2,21 m	3,83 m2	
Emprise equipements		3,83 m2	11 %

Section 2 / 2 - Table

Surface 12,10 m2 - perimetre 14,06 m - pin-classe4

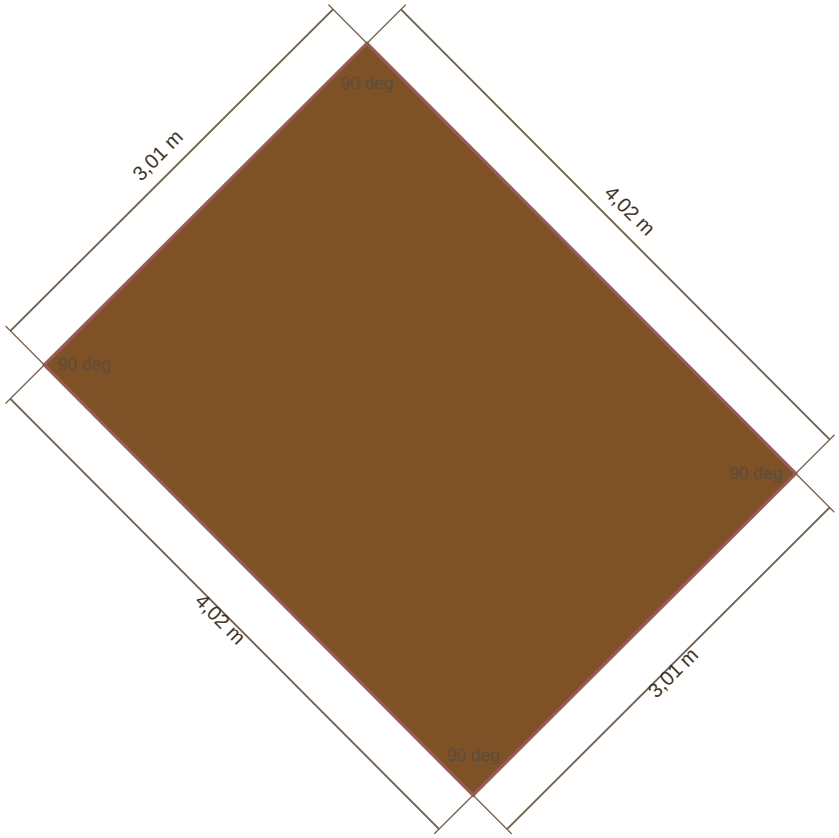

Echelle 1/50

0 2 m

Dimensions

Element	Cote / emprise	Surface	Angle au depart
Cote 1	3,01 m		90 deg
Cote 2	4,02 m		90 deg
Cote 3	3,01 m		90 deg
Cote 4	4,02 m		90 deg
Terrasse Table	perimetre 14,06 m	12,10 m2	4 sommets