

Plan interactif - Parcelle AE 101

Echelle 1/200 - genere le 21/09/2026 - Plan interactif v1.2.0-alpha.2

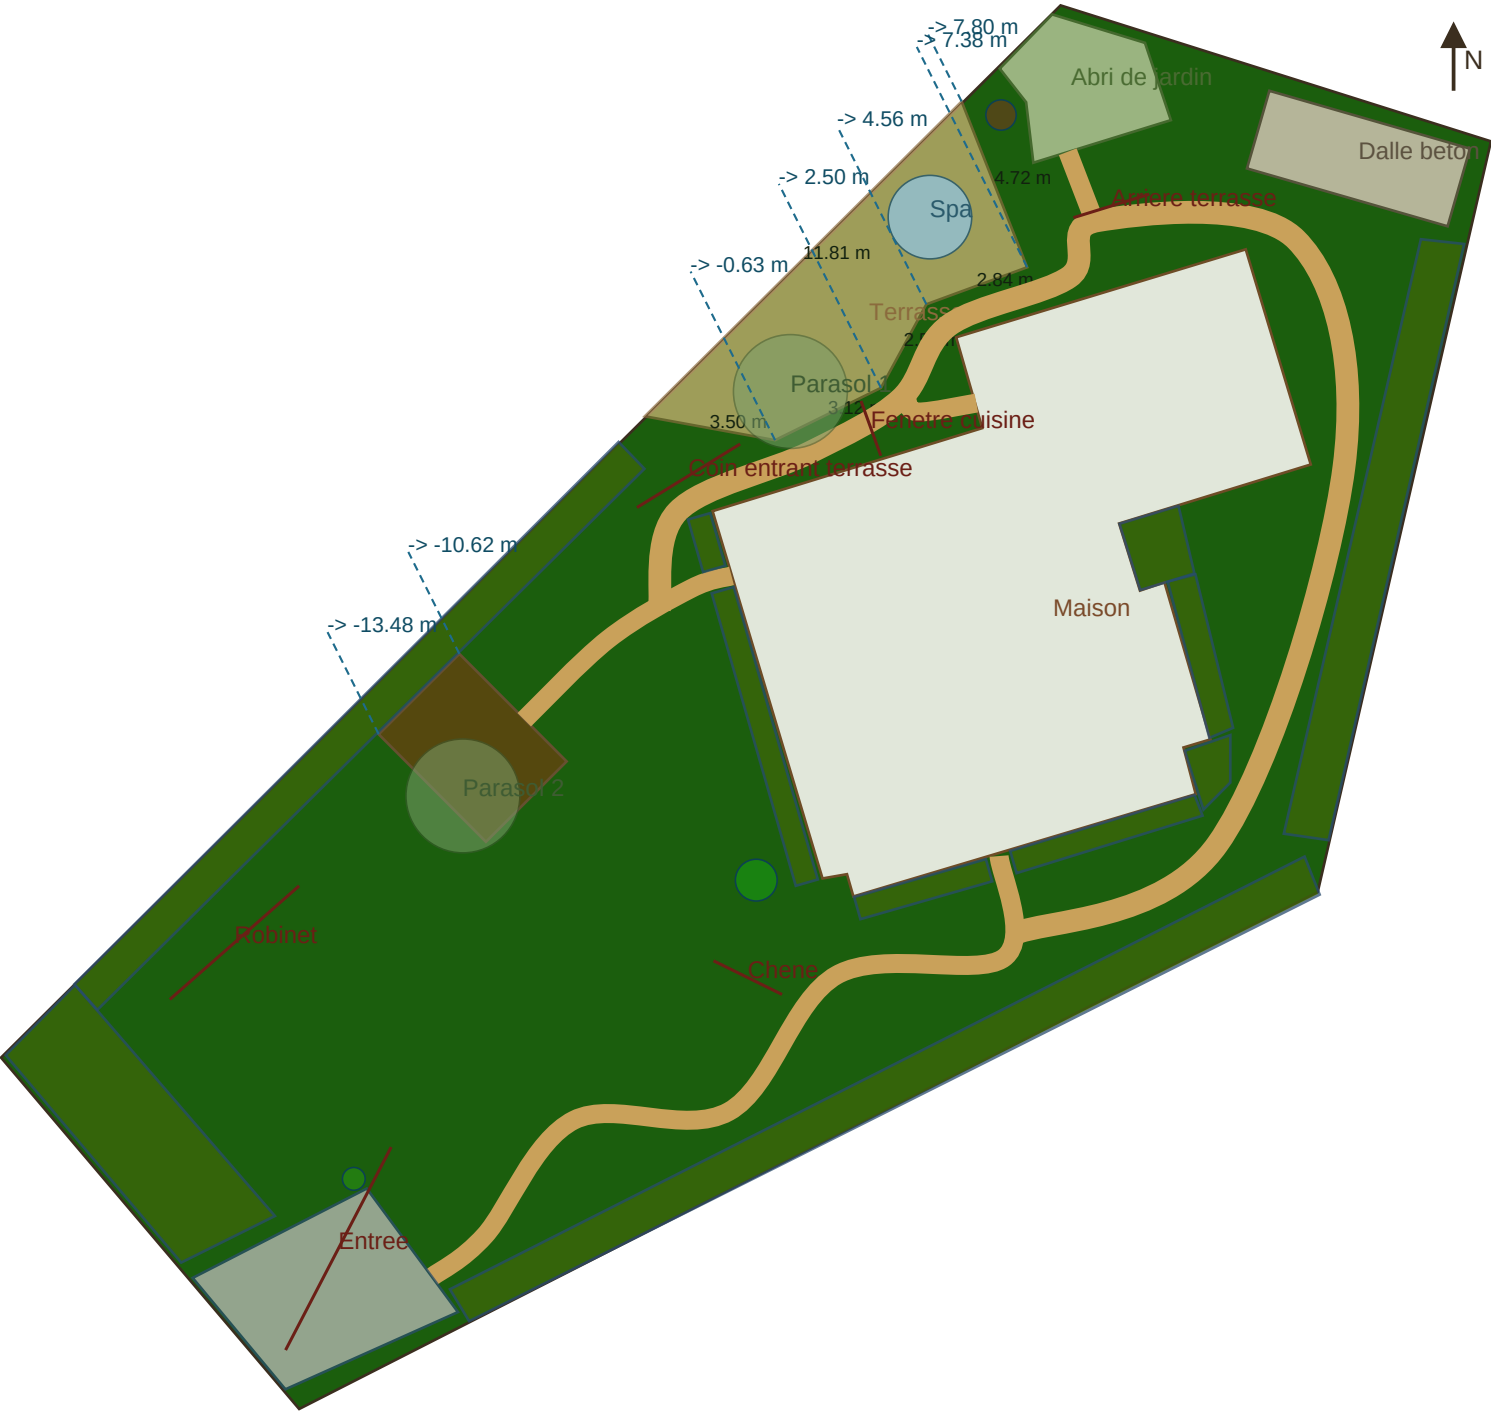


Tableau des surfaces

Objet	Surface	% parcelle
Parcelle AE 101	722.99 m2	-
Terrasse	35.01 m2	4.8 %
Chemin Arriere	26.84 m2	3.7 %
Maison	151.78 m2	21.0 %
Dalle beton	11.81 m2	1.6 %
Abri de jardin	11.00 m2	1.5 %
Chemin ZigZag	10.78 m2	1.5 %
Spa	3.83 m2	0.5 %
Table	12.10 m2	1.7 %
Parking	19.61 m2	2.7 %
Chemin Table	3.40 m2	0.5 %
Chemin Buandrie	1.00 m2	0.1 %
Chene	0.96 m2	0.1 %
Erbale	0.51 m2	0.1 %
Abri de jardin Chemin	0.94 m2	0.1 %
Arbre Entree	0.29 m2	0.0 %
Coin entrant terrasse	0.26 m2	0.0 %
Arriere terrasse	0.17 m2	0.0 %
Fenetre cuisine	0.12 m2	0.0 %
Parasol 1	7.13 m2	1.0 %
Parasol 2	7.13 m2	1.0 %
Entree	0.49 m2	0.1 %
Robinet	0.37 m2	0.1 %
Chene	0.16 m2	0.0 %
Plattebande Rue	20.18 m2	2.8 %
Platebande Aline	19.26 m2	2.7 %
Platebande Joel	26.01 m2	3.6 %
Platebande Guitare	18.86 m2	2.6 %
Platebande Cuisine Petit Salon	4.87 m2	0.7 %
Plattebande Cuisine	0.88 m2	0.1 %
Platebande PEtit Salon Entree	2.21 m2	0.3 %
Platebande Grand Salon Entree	3.05 m2	0.4 %
Platebande grand Salon Arriere	3.02 m2	0.4 %
Platebande Angle Grand Salon	1.49 m2	0.2 %
Platebande Grand Salon Clim	2.87 m2	0.4 %
Emprise totale hors parcelle	408.37 m2	56.5 %